
Construction Area for Water Distribution Pipe Replacement Work in the Doyomaru (Koreishi) District and Surrounding Areas



Schematic Plan of Final Pavement Restoration Areas

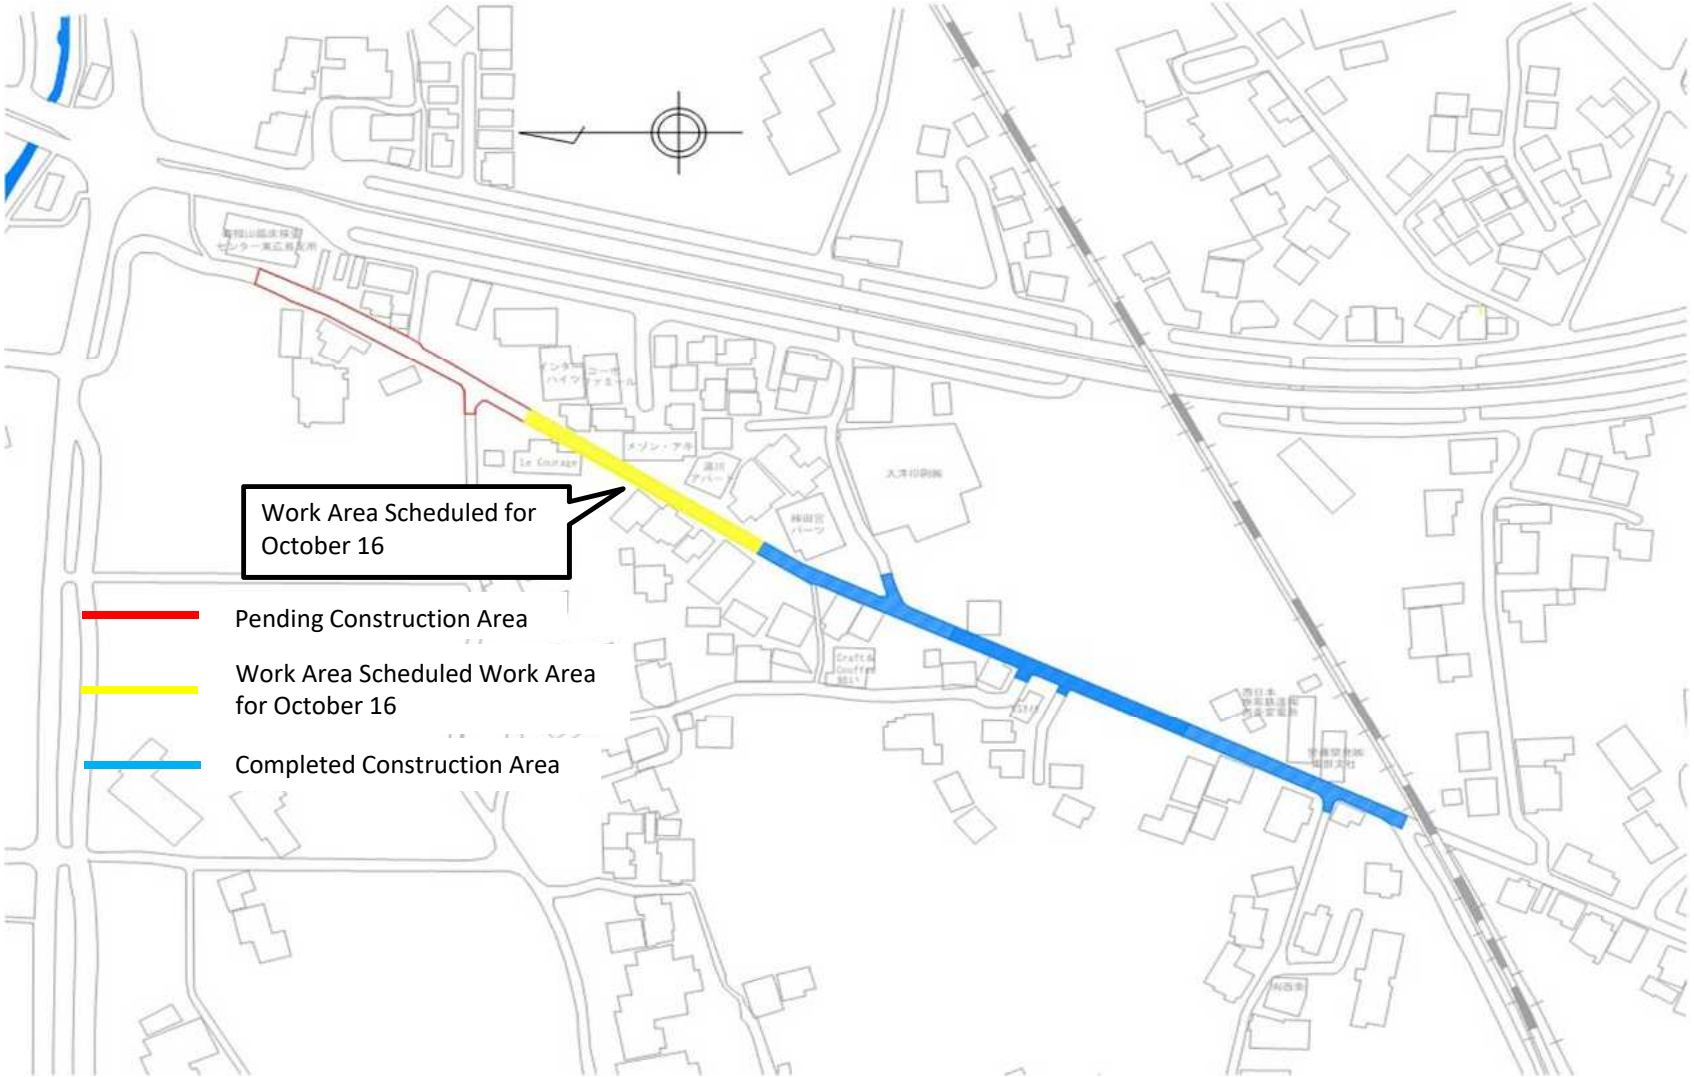


Final Pavement Restoration: Approx. 1,072.7 m²

Completed: 563.7 m²

Final Pavement Restoration Progress: 52.5%

Traffic Restriction Area (October 16)

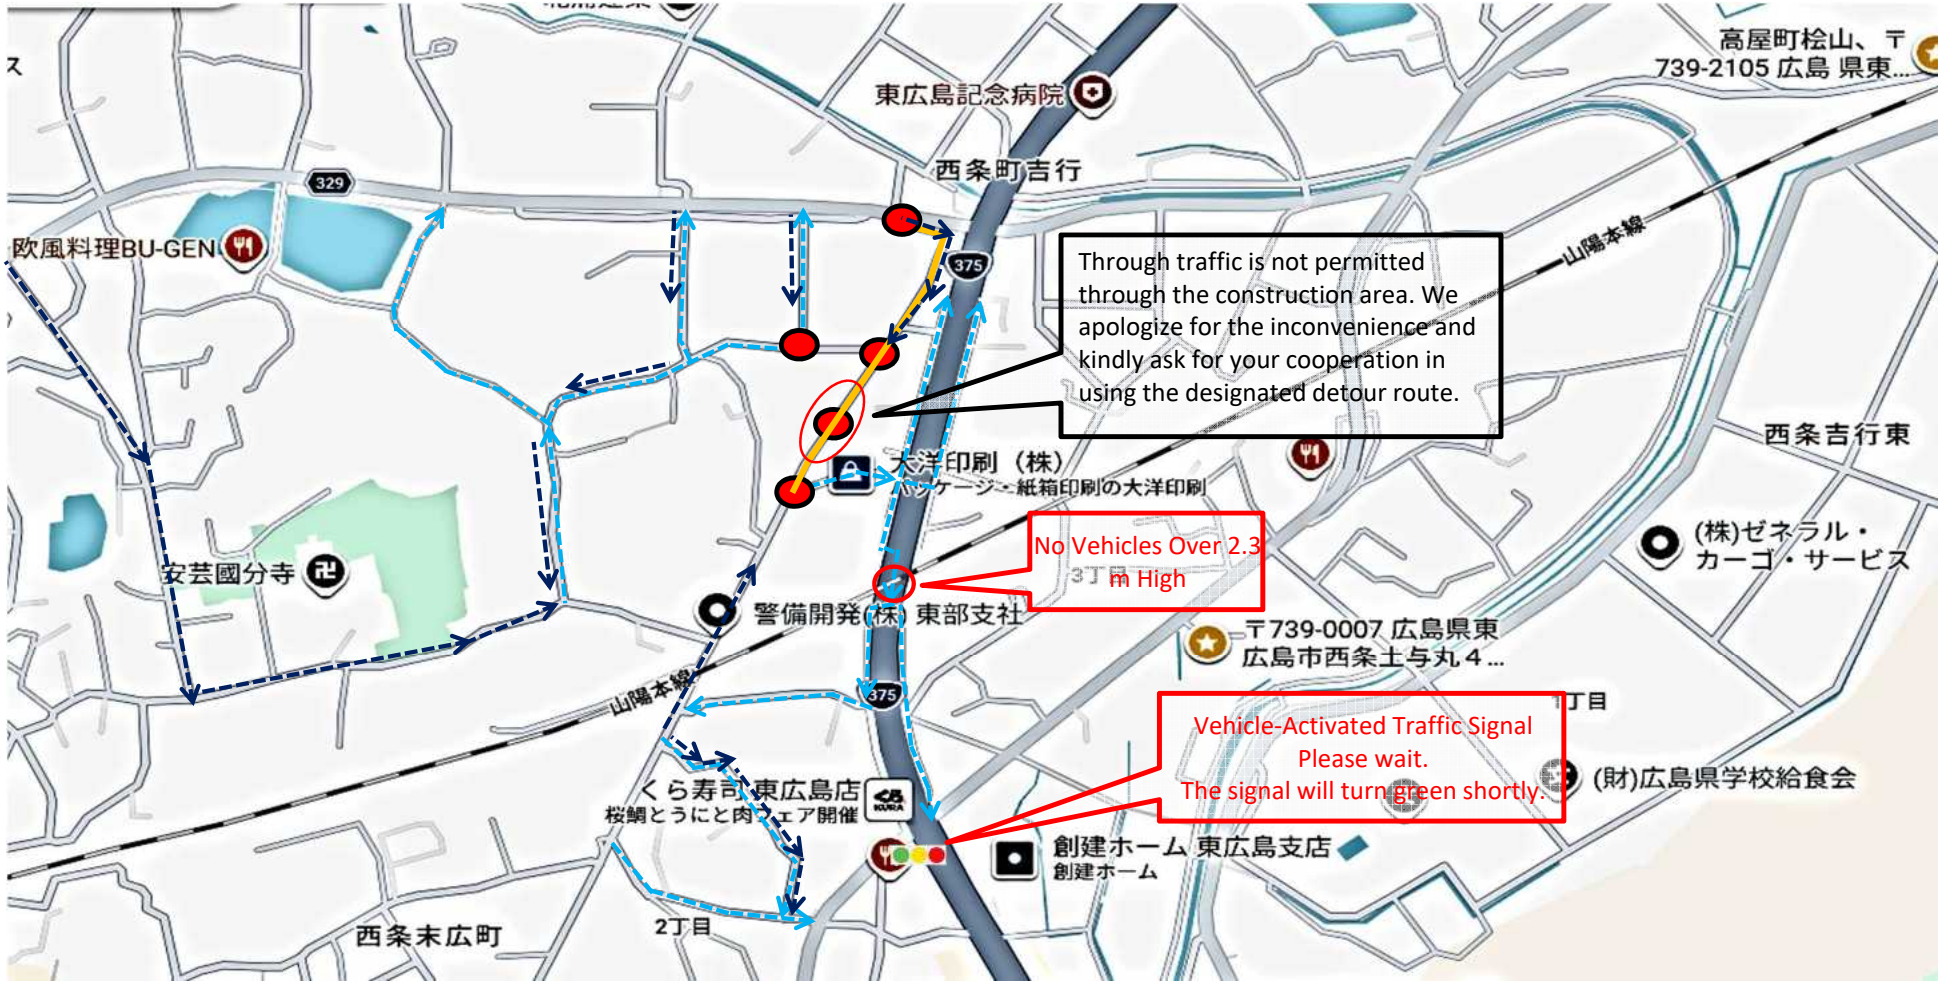

Planned Traffic Guide Location

Construction Road Closure Area

Detour

Drivers of medium-sized vehicles are kindly requested to select the appropriate route according to their destination. Thank you for your cooperation.(Right turn prohibited from the Kura Sushi direction between 7:00 AM and 9:00 AM.)