


Construction Area for Water Distribution Pipe Replacement Work in the Doyomaru (Koreishi) District and Surrounding Areas

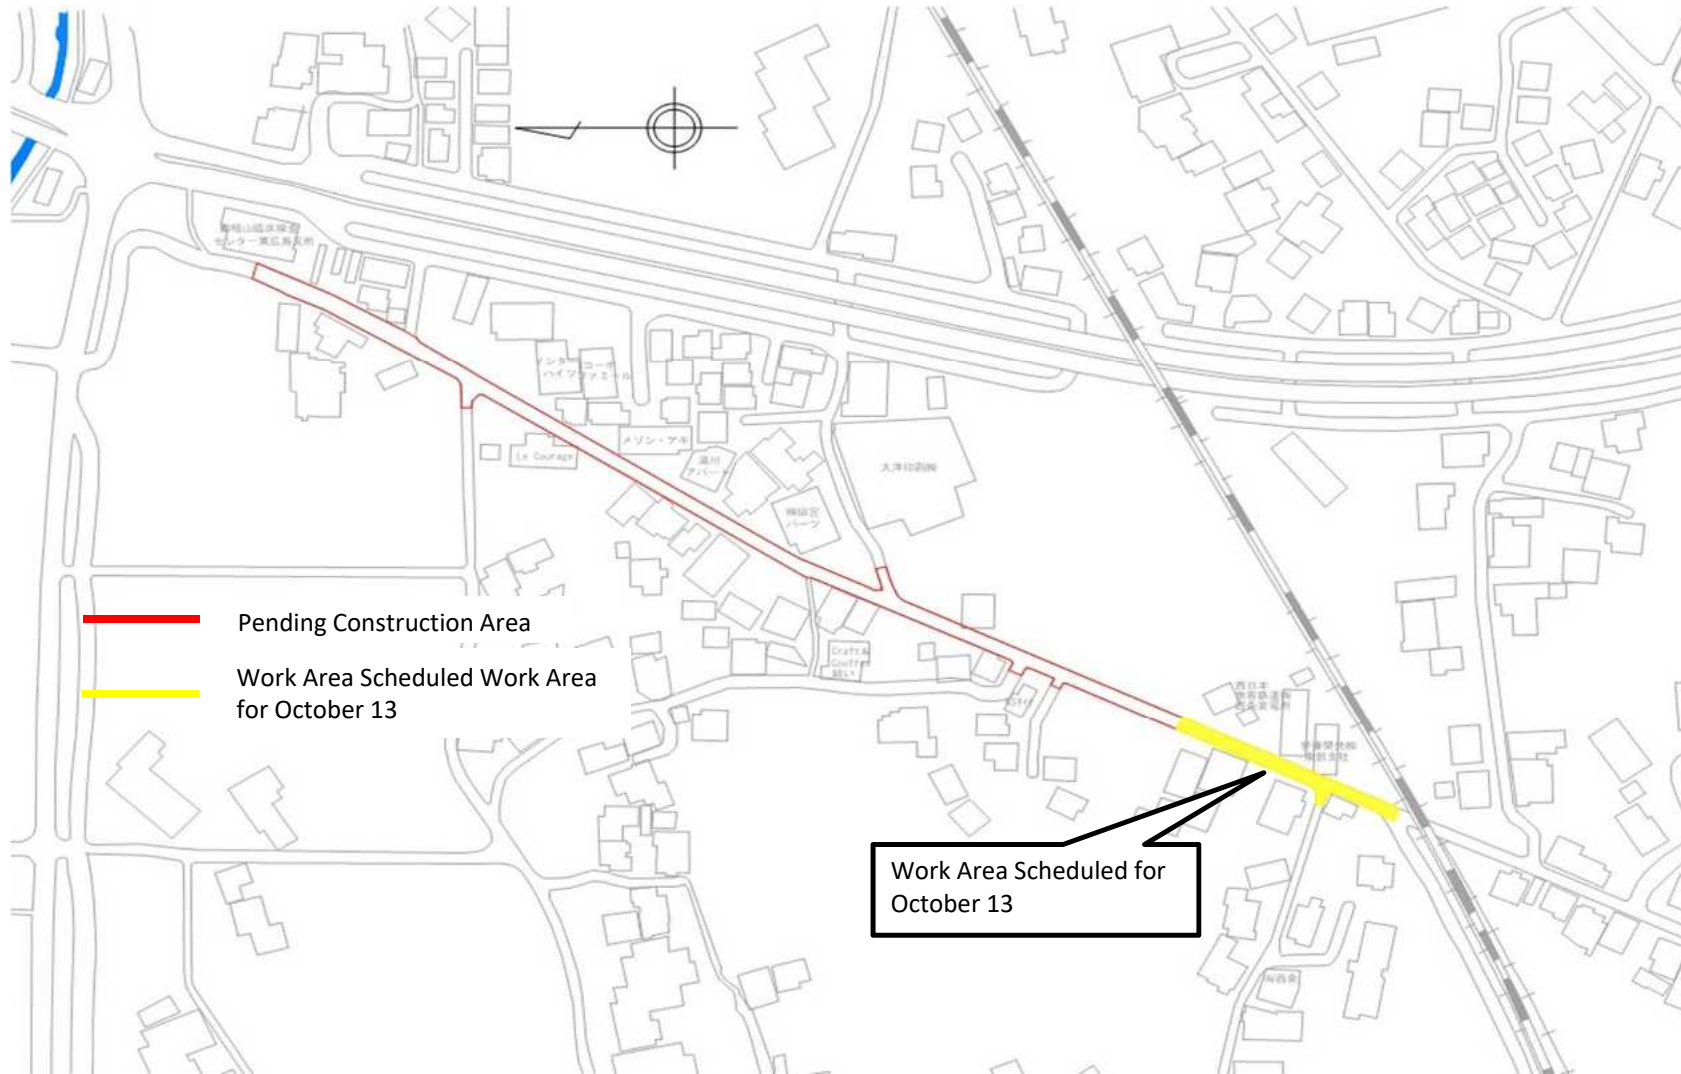

Schematic Plan of Final Pavement Restoration Areas




Final Pavement Restoration: Approx. 1,072.7 m²

Completed: 0 m²

Final Pavement Restoration
Progress: 0%

Traffic Restriction Area (October 13)

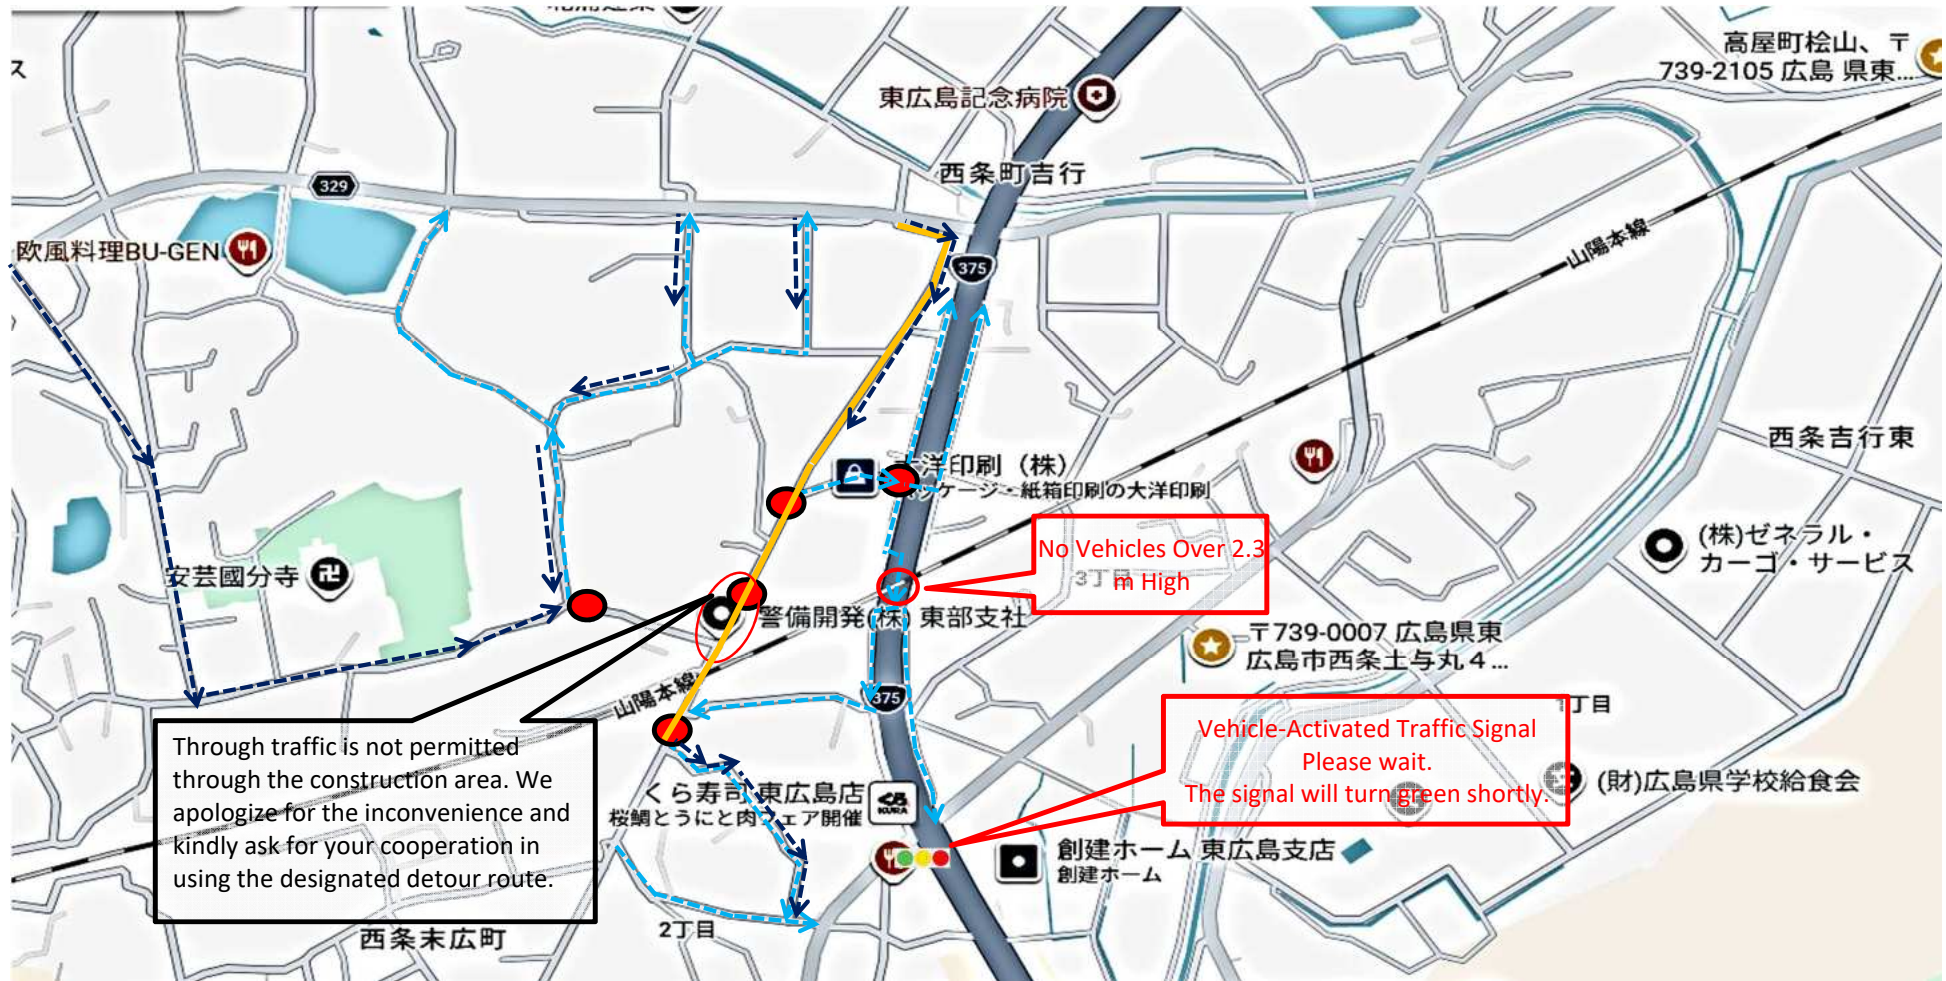

- Planned Traffic Guide Location
- Construction Road Closure Area
- - - Detour
- - - Drivers of medium-sized vehicles are kindly requested to select the appropriate route according to their destination. Thank you for your cooperation. (Right turn prohibited from the Kura Sushi direction between 7:00 AM and 9:00 AM.)